


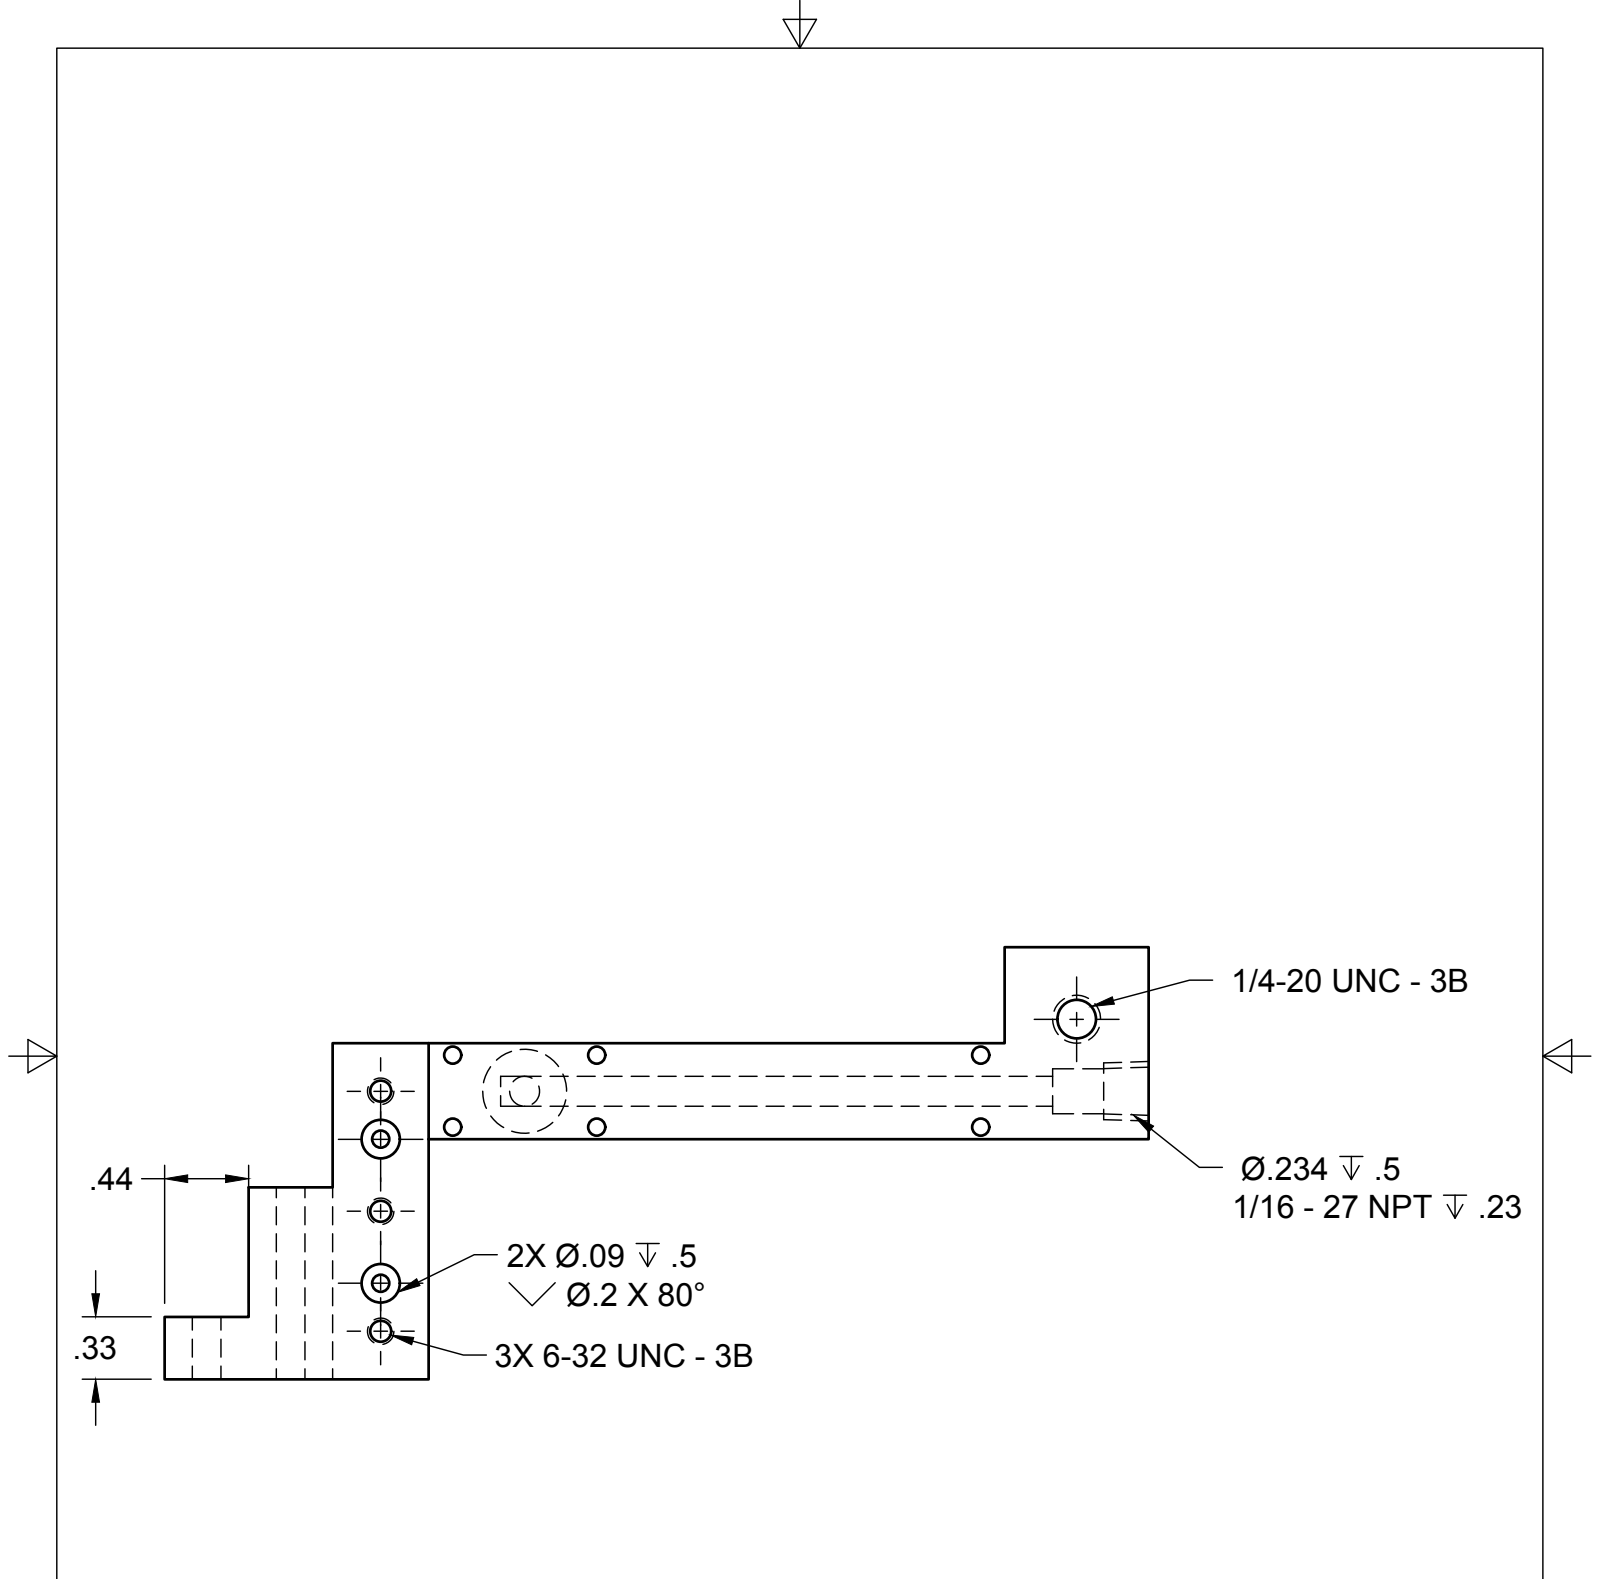

		PROJECT			
		Bitter Coil 2024			
		TITLE			
		Bus-Bar-System			
APPROVED		SIZE	CODE	DWG NO	REV
CHECKED		A			
DRAWN	Henry Ando	5/6/25	SCALE 1:1	WEIGHT	SHEET 1/1